
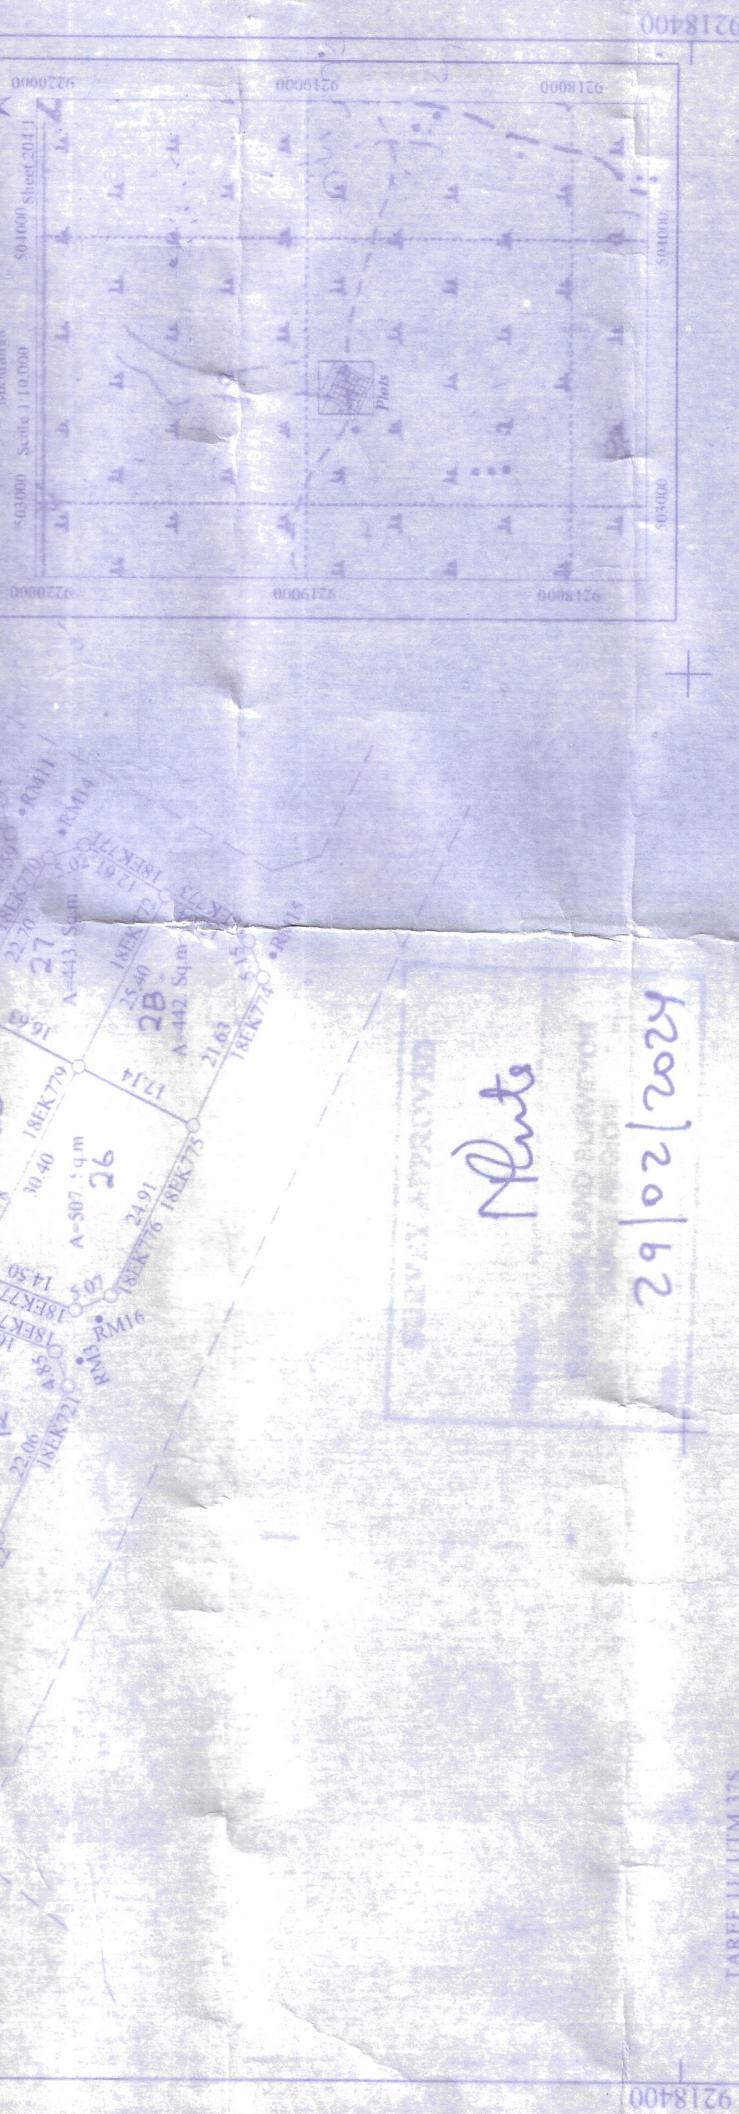


**SURVEY OF PLOTS NO. 1 - 28 BLOCK "P" AT HOMBOZA
KISARAWE DISTRICT COUNCIL COAST REGION.**

503500 503600

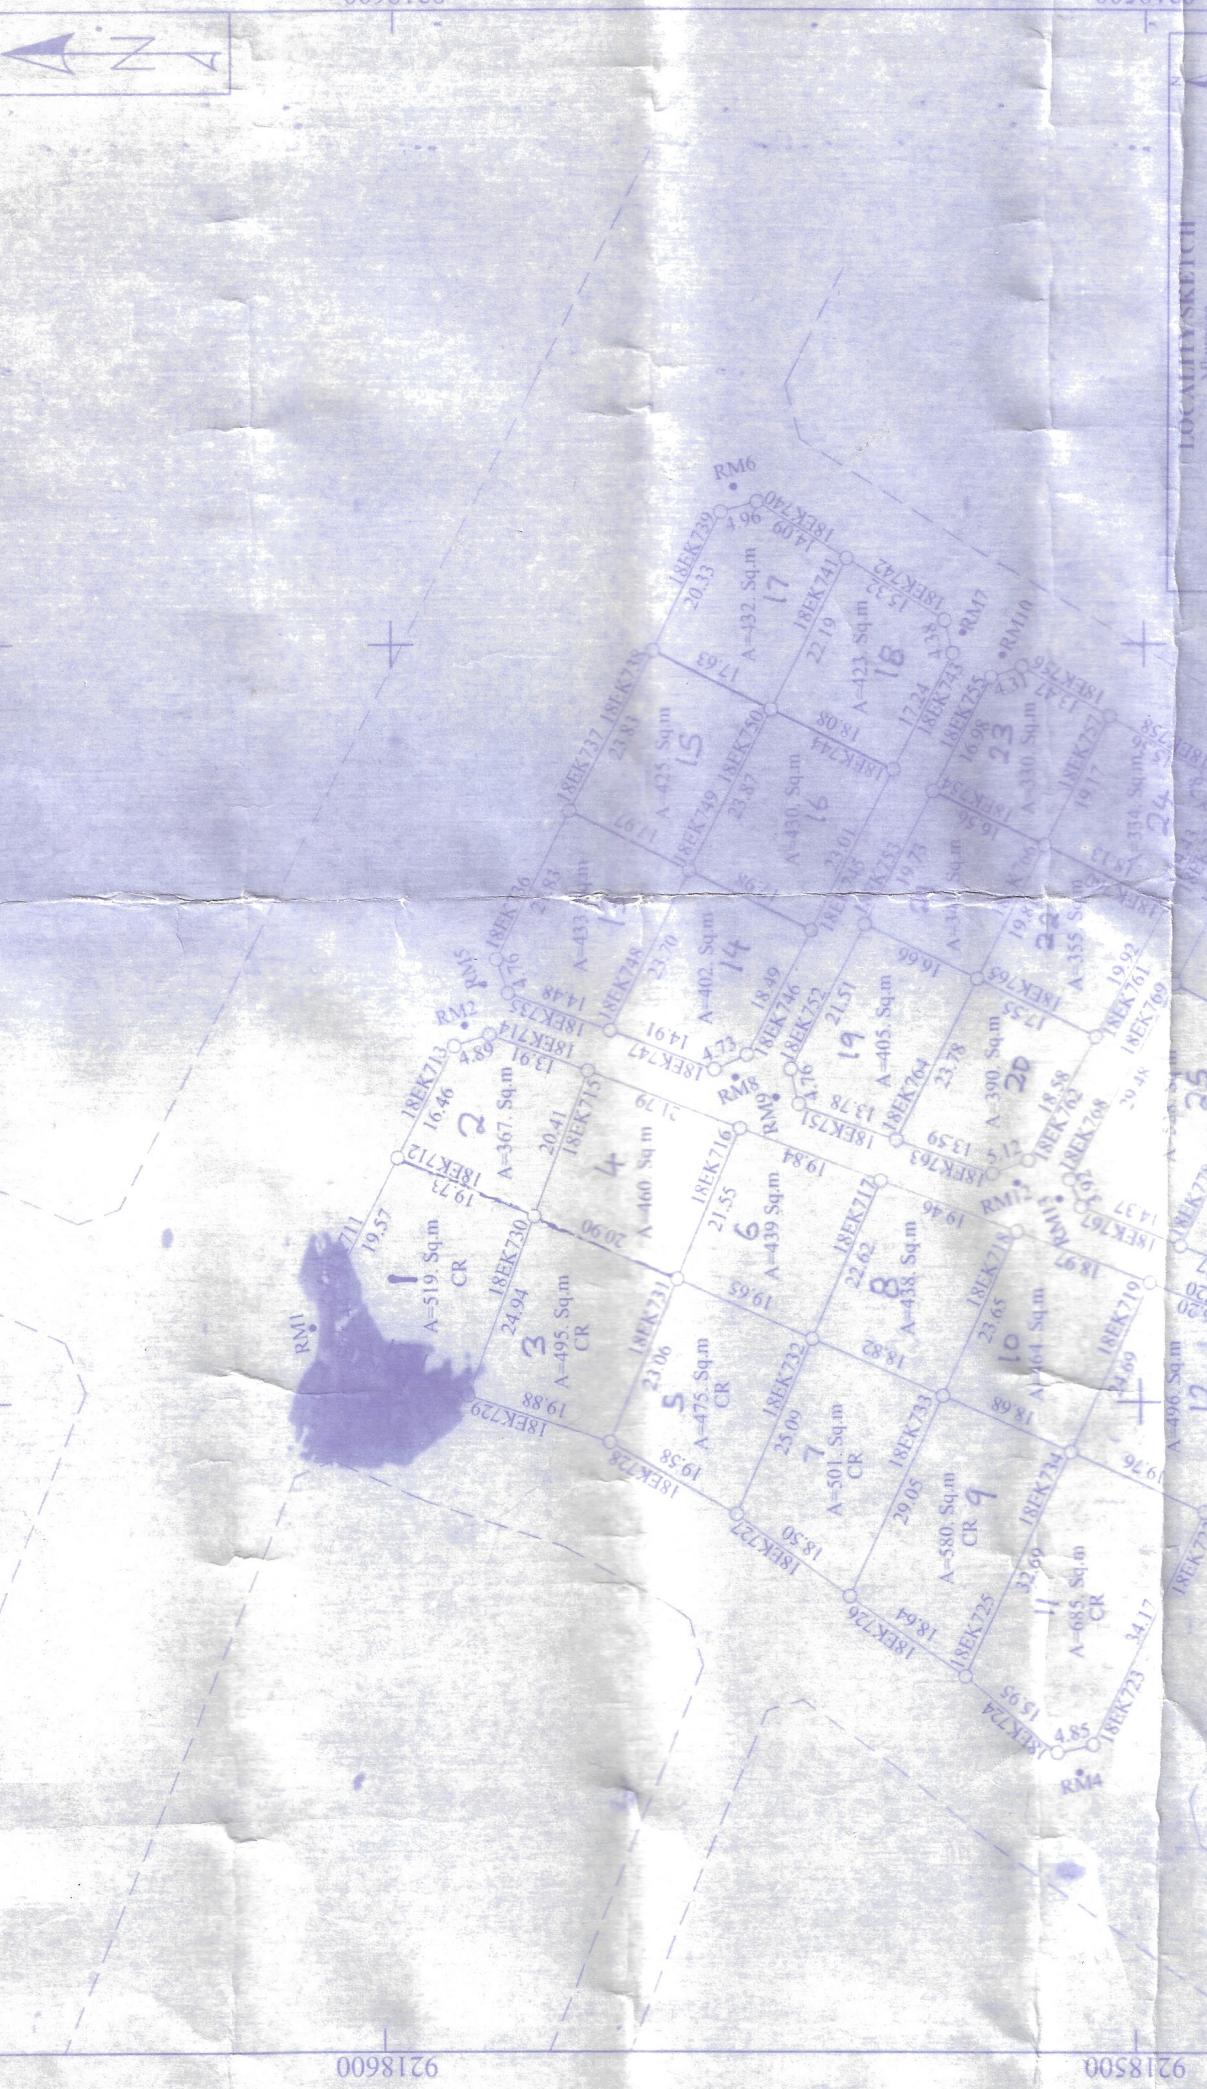

TAREF 11 UTM 31S Refer to TP Dwg No 19 KSW/421/042023		SCALE 1:1000	503600
Comps No. E 370B	AMENDMENTS MADE BY Mashaka, N (Plot No. 29-2-2624)	Plan drawn by S. Kelvin I hereby certify that the survey represented by this plan was carried out in accordance with the survey regulations.	
M.P. No. 204/119	Std Sheet 204/1	W <u>24</u> - 24-02-2024	
Action C	PHOTOS AT COPIES SENT TO: JOVITUS F. KAMUZORA LICENSED LAND SURVEYOR WORLD MAP INTERNATIONAL LTD Registered Plan No. 191137		
Plan No. E 370/EB			